


CORPORATE / LEVEL 01

Advisory / client reception / corporate commons • One floor shown • North is up

CONCEPT REVIEW / R02
SH-SITE-0001-A-L01 / SH-MAP-SAC-024

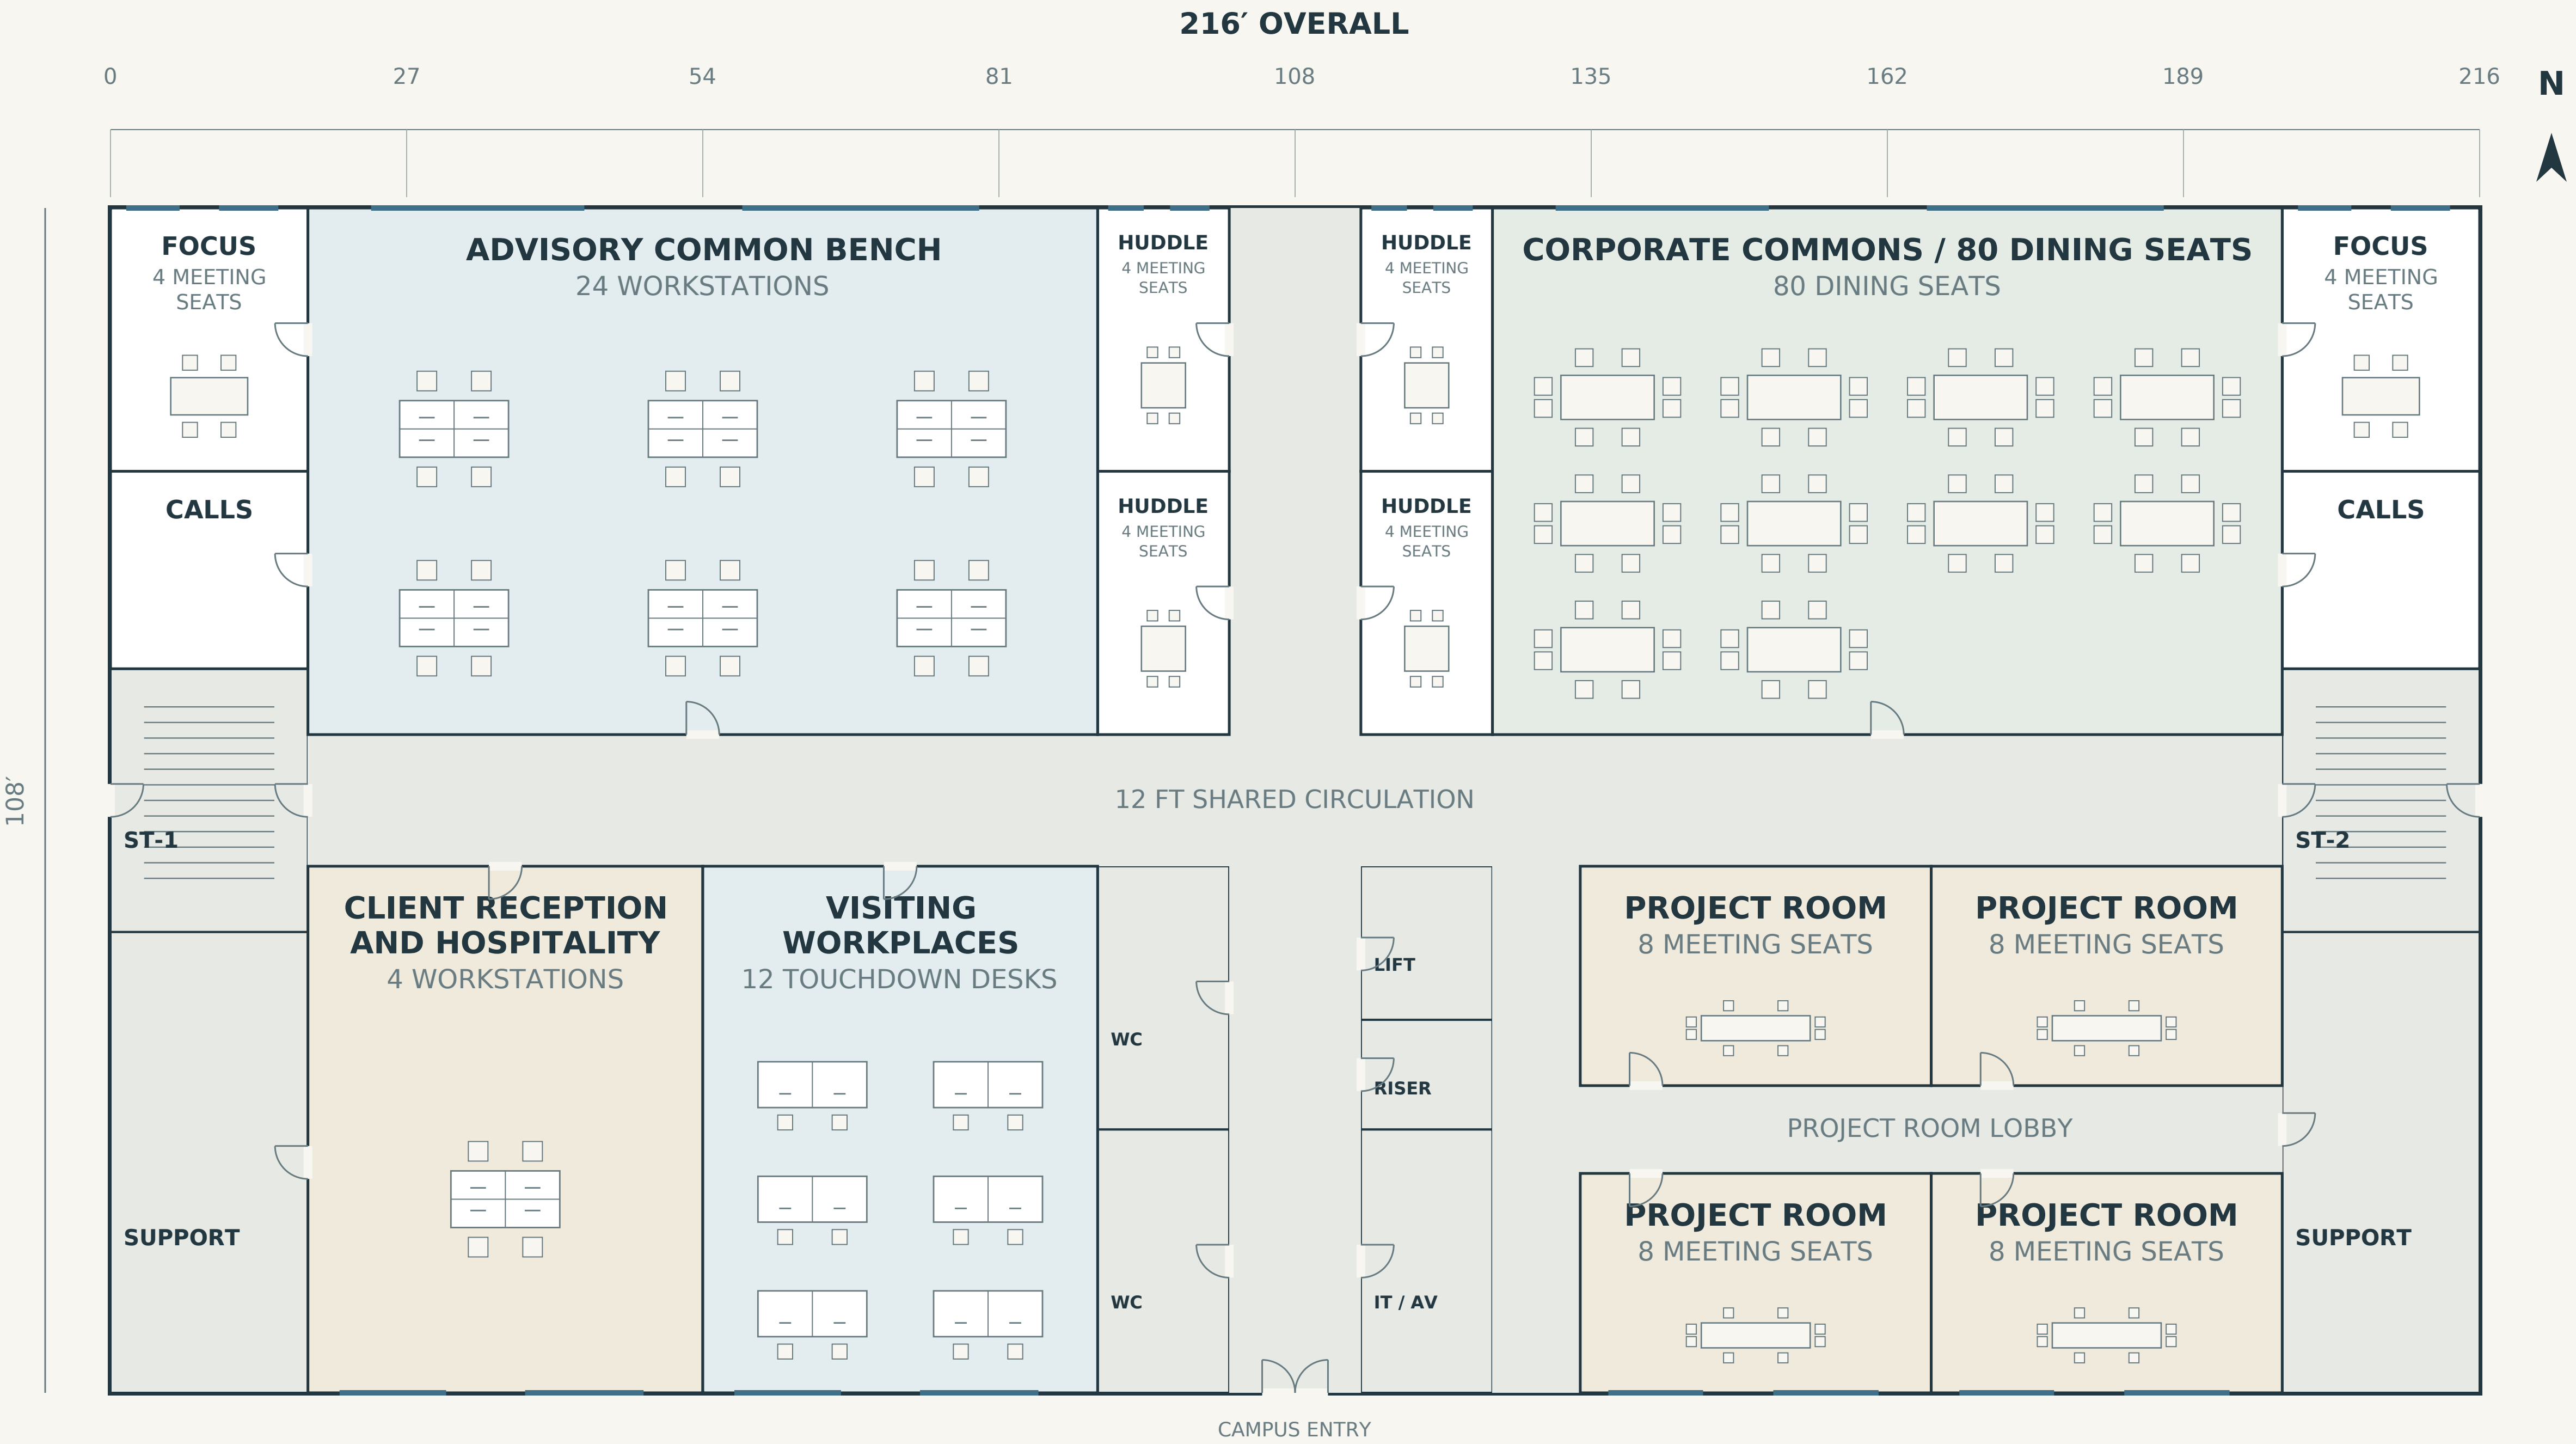

THIS FLOOR

40

FITTED WORKPLACES

23,328

GROSS SQUARE FEET

FLOOR PROGRAM

Advisory common bench • Client reception and hospitality • Visiting workplaces

INSTITUTIONAL BOUNDARY

Board governs, CEO directs and ESS administers shared services. Internal Audit retains independently controlled Board access; J2 and business product organizations retain their separate authority.

DESIGN LOAD / STATUS


23,328 gross sq ft; 52 planned concurrent occupants. R02 concept only; actual staffing, occupancy and construction remain unestablished.

01 SHARED CAMPUS

24 Advisory shared desks + 4 reception workplaces + 12 visiting workplaces = 40 fitted staff workplaces.

02 CONTROLLED ACCESS

Corporate commons has 80 dining seats, supplied from the single production kitchen in C; no second production kitchen.

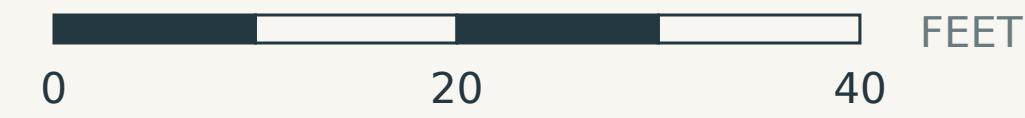

Blue: staff work / Sage: shared or independent program / Sand: visitor and project rooms