


J2 / LEVEL 02

Judgment / Orientation / J2 headquarters • One floor shown • North is up

CONCEPT REVIEW / R02

SH-SITE-0001-B-L02 / SH-MAP-SAC-029

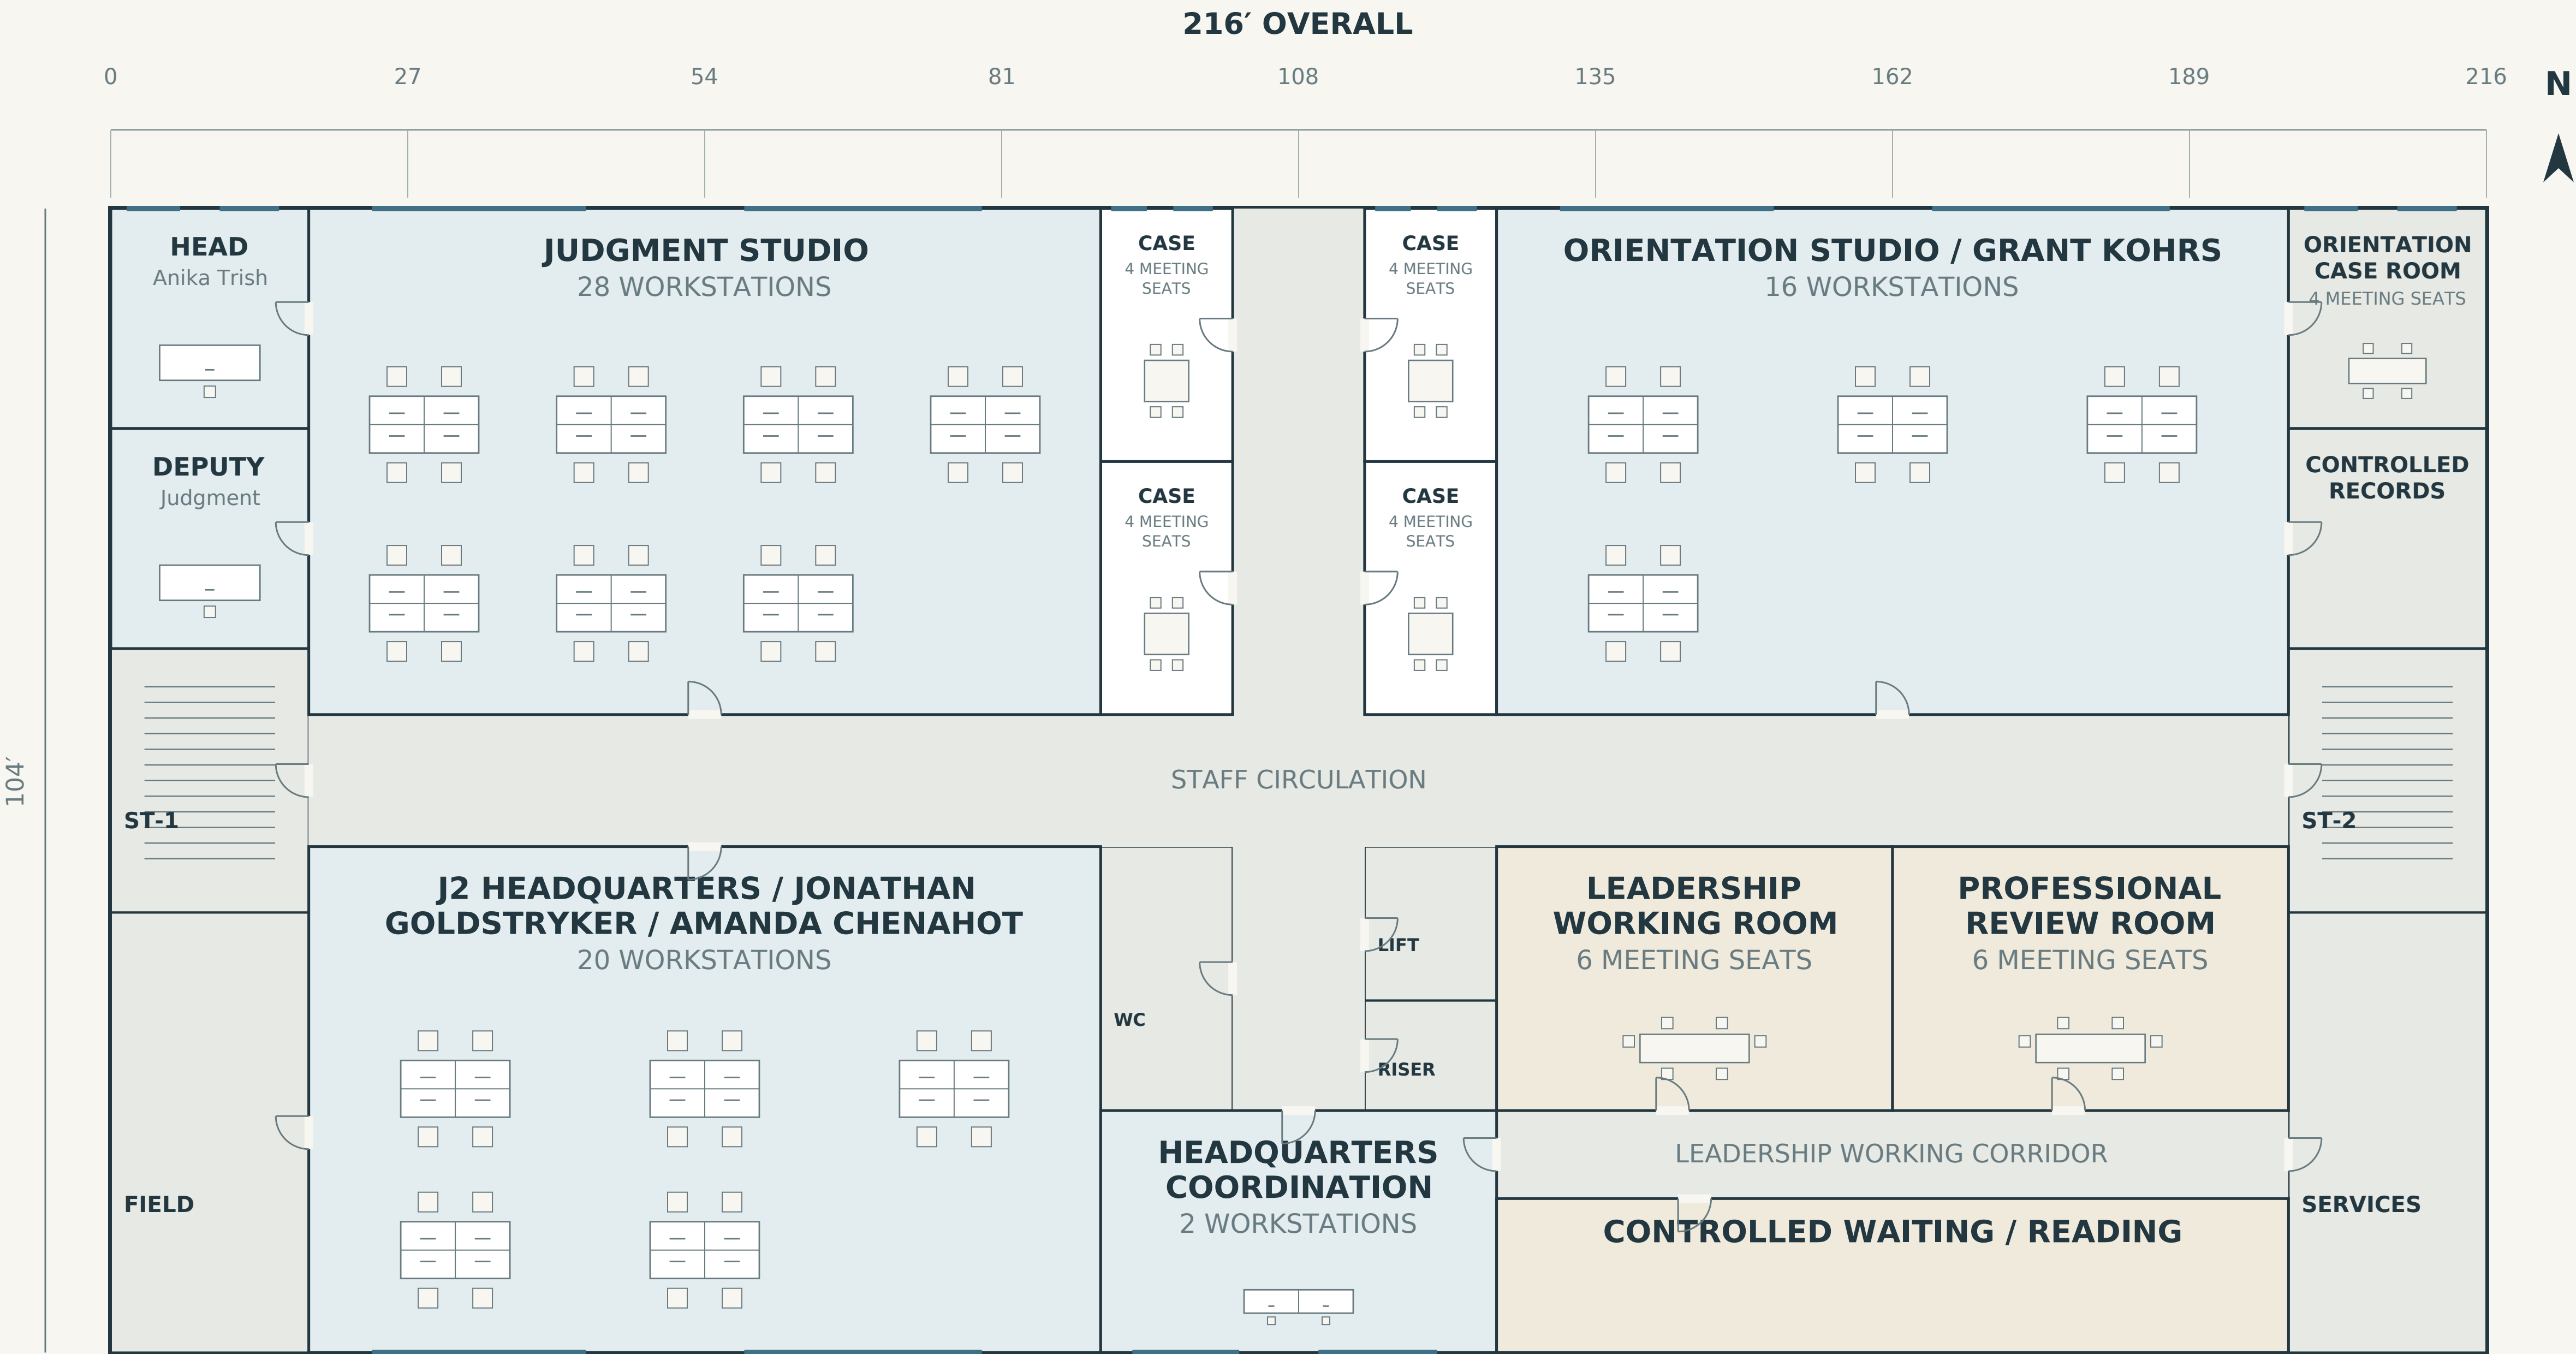

THIS FLOOR

68

FITTED WORKPLACES

22,464

GROSS SQUARE FEET

FLOOR PROGRAM

Head of Judgment / Anika Trish · Deputy Head of Judgment · Judgment studio · Orientation studio / Grant Kohrs · J2 headquarters / Jonathan Goldstryker / Amanda Chenahot · Headquarters coordination

INSTITUTIONAL BOUNDARY

Board governs, CEO directs and ESS administers shared services. Internal Audit retains independently controlled Board access; J2 and business product organizations retain their separate authority.

DESIGN LOAD / STATUS


22,464 gross sq ft; 68 planned concurrent occupants. R02 concept only; actual staffing, occupancy and construction remain unestablished.

01 PROFESSIONAL WORK

30 Judgment desks include Head/Deputy; 16 Orientation and 22 Headquarters desks complete 68 fitted workplaces.

02 ONE AUTHORIZATION

J2 building 130 workplaces are not 237 authorized billets; Education 35 remains included in 237, in C.

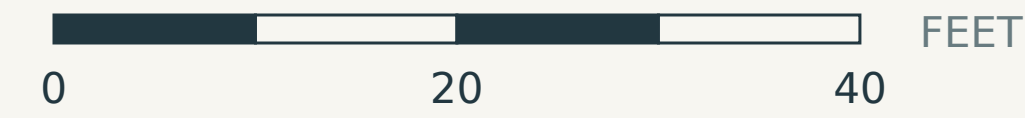

Blue: Judgment, Orientation and J2 HQ / Sand: shared project rooms