


EDUCATION / LEVEL 02

Faculty / case design / executive simulations • One floor shown • North is up

CONCEPT REVIEW / R02

SH-SITE-0001-C-L02 / SH-MAP-SAC-032

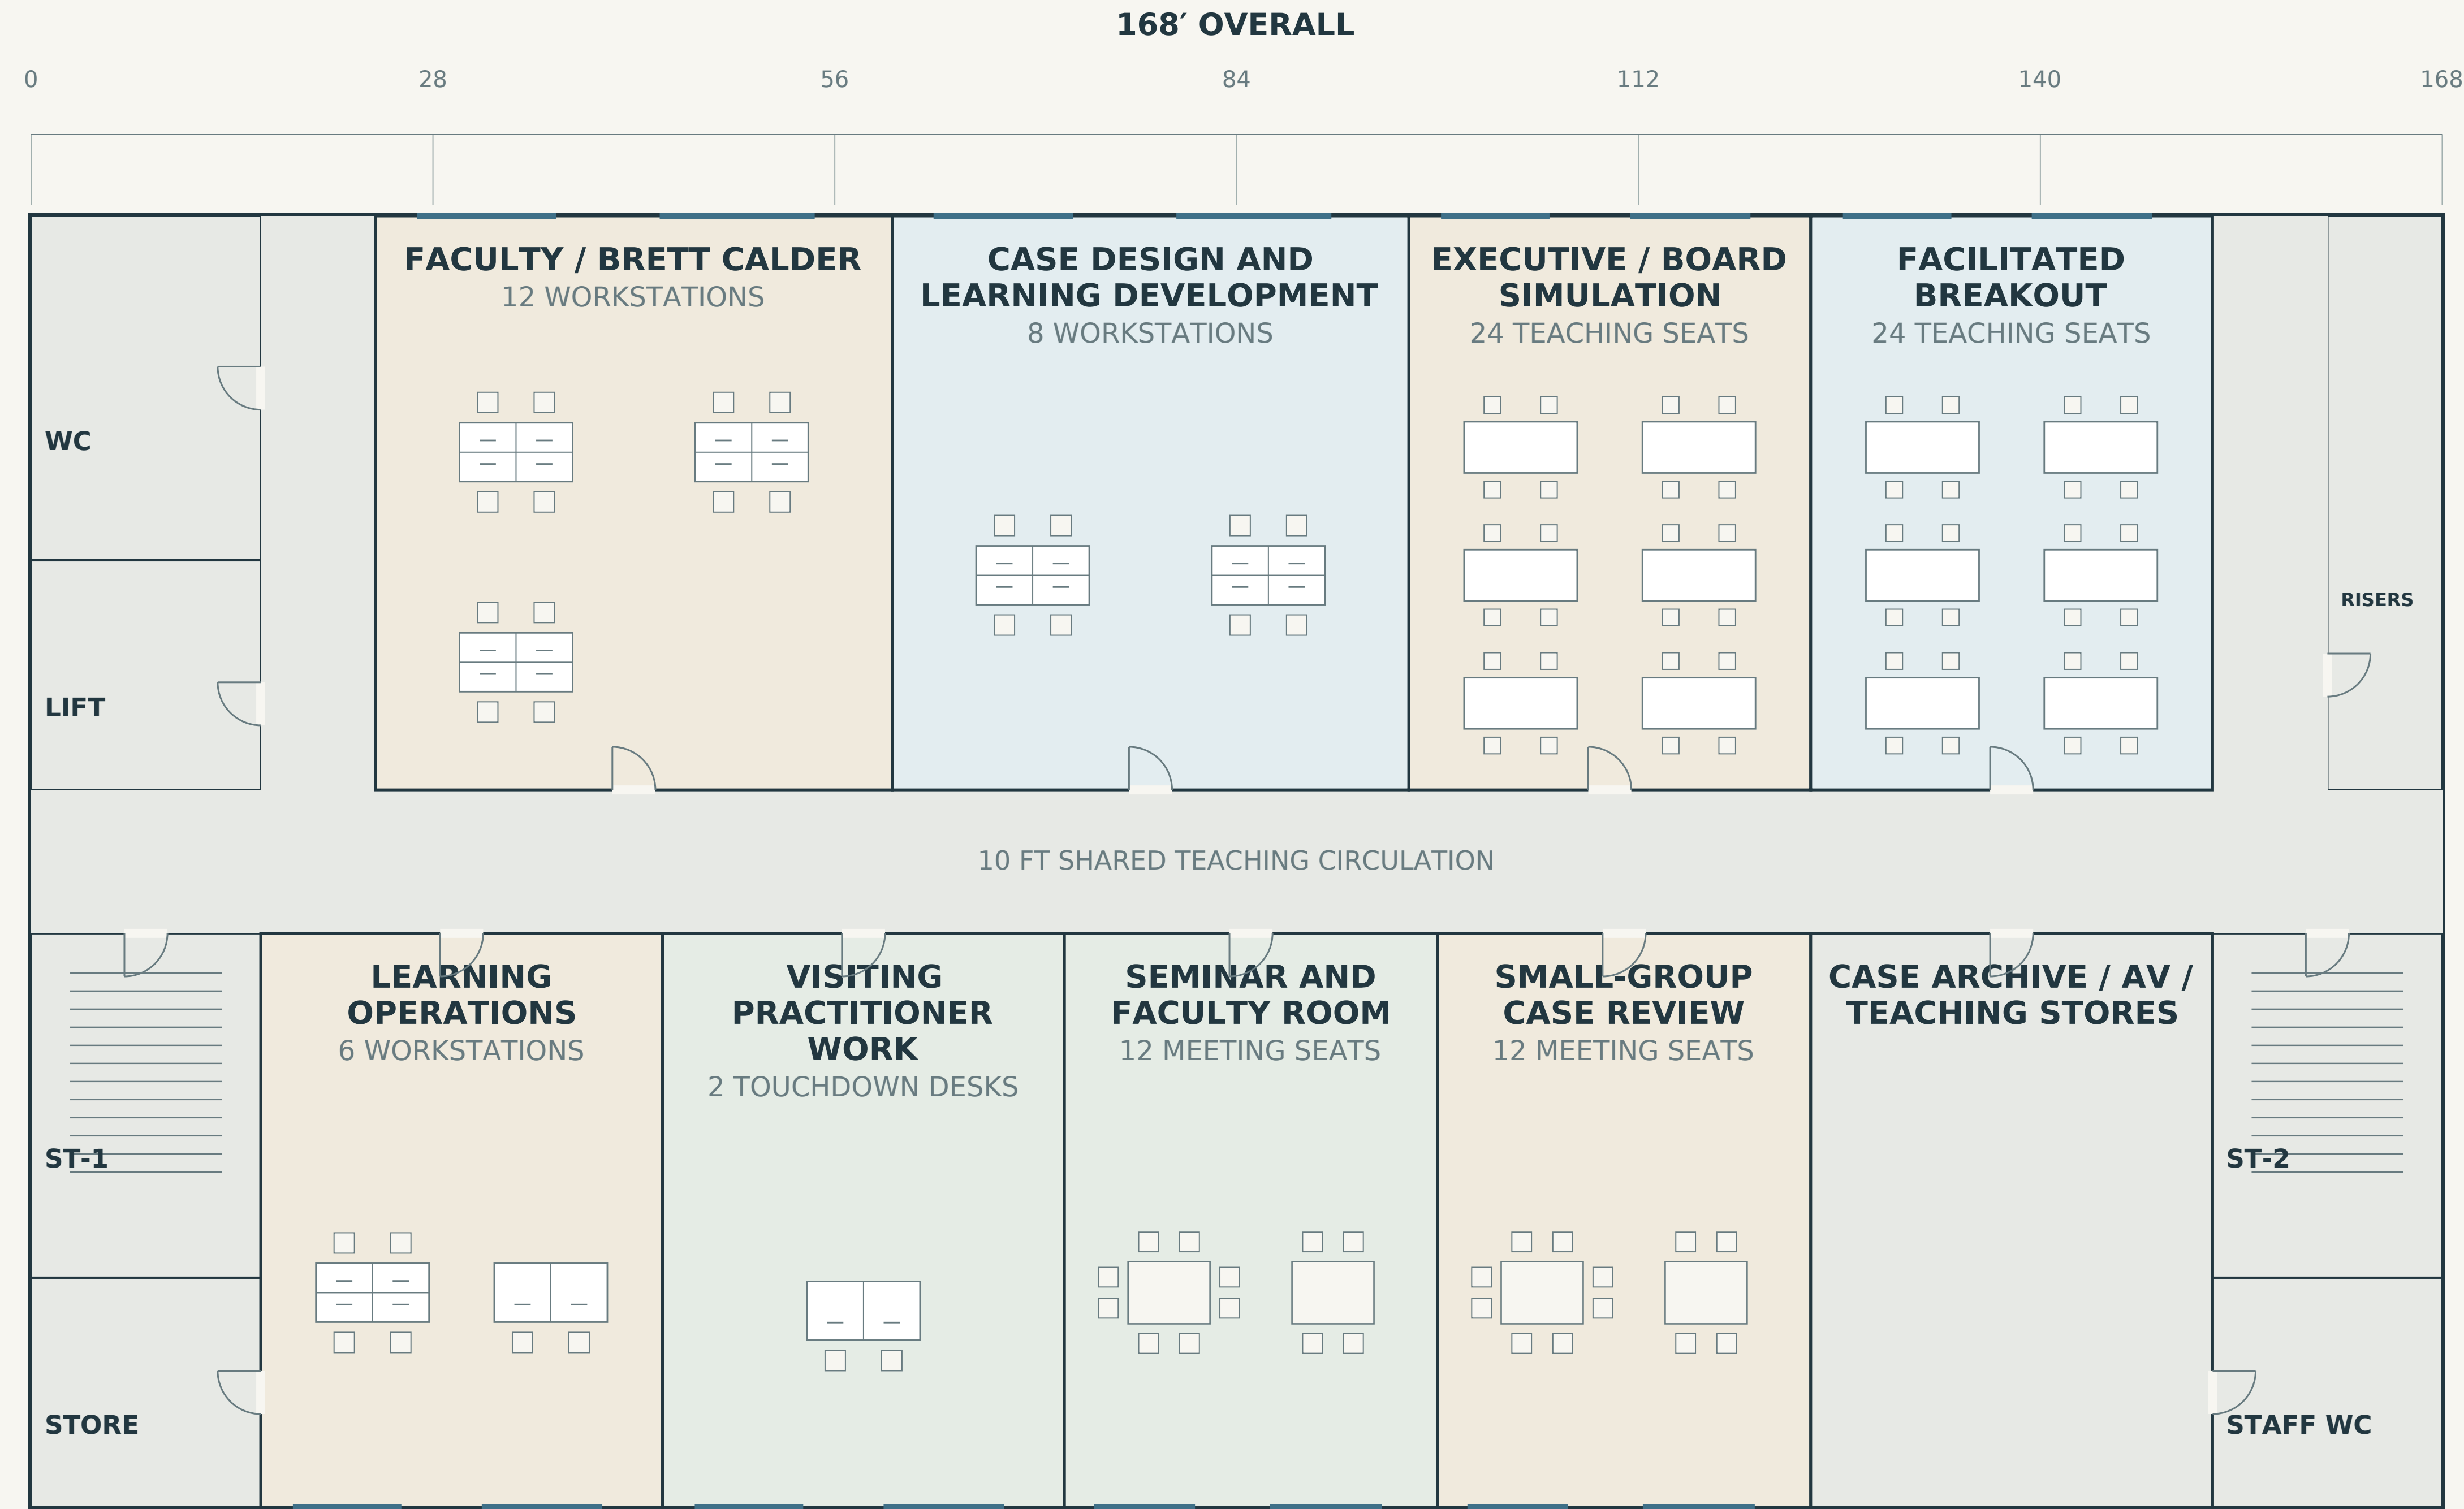

THIS FLOOR

28

FITTED WORKPLACES

15,120

GROSS SQUARE FEET

FLOOR PROGRAM

Faculty / Brett Calder • Case design and learning development • Learning operations • Visiting practitioner work

INSTITUTIONAL BOUNDARY

Board governs, CEO directs and ESS administers shared services. Internal Audit retains independently controlled Board access; J2 and business product organizations retain their separate authority.

DESIGN LOAD / STATUS


15,120 gross sq ft; 28 planned concurrent occupants. R02 concept only; actual staffing, occupancy and construction remain unestablished.

01 ONE EDUCATION ARM

28 upstairs desks: 12 faculty, 8 design, 6 learning operations and 2 visiting practitioner workplaces.

02 TEACHING SUPPORT

Upstairs simulations and breakout seats share the 120 learner campus cap; they do not create additional cohorts.

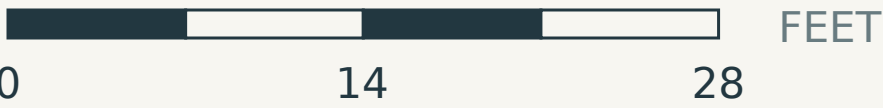

Blue: design and teaching / Sage: visiting work / Sand: faculty and meetings