


TAYLOR WAREHOUSE / LEVEL 01

Taylor warehouse — ground level • One floor shown • North is up

CONCEPT REVIEW / R02

SH-IND-FAC-TAY-WAREHOUSE-B01-L01 / SH-MAP-ARU-029

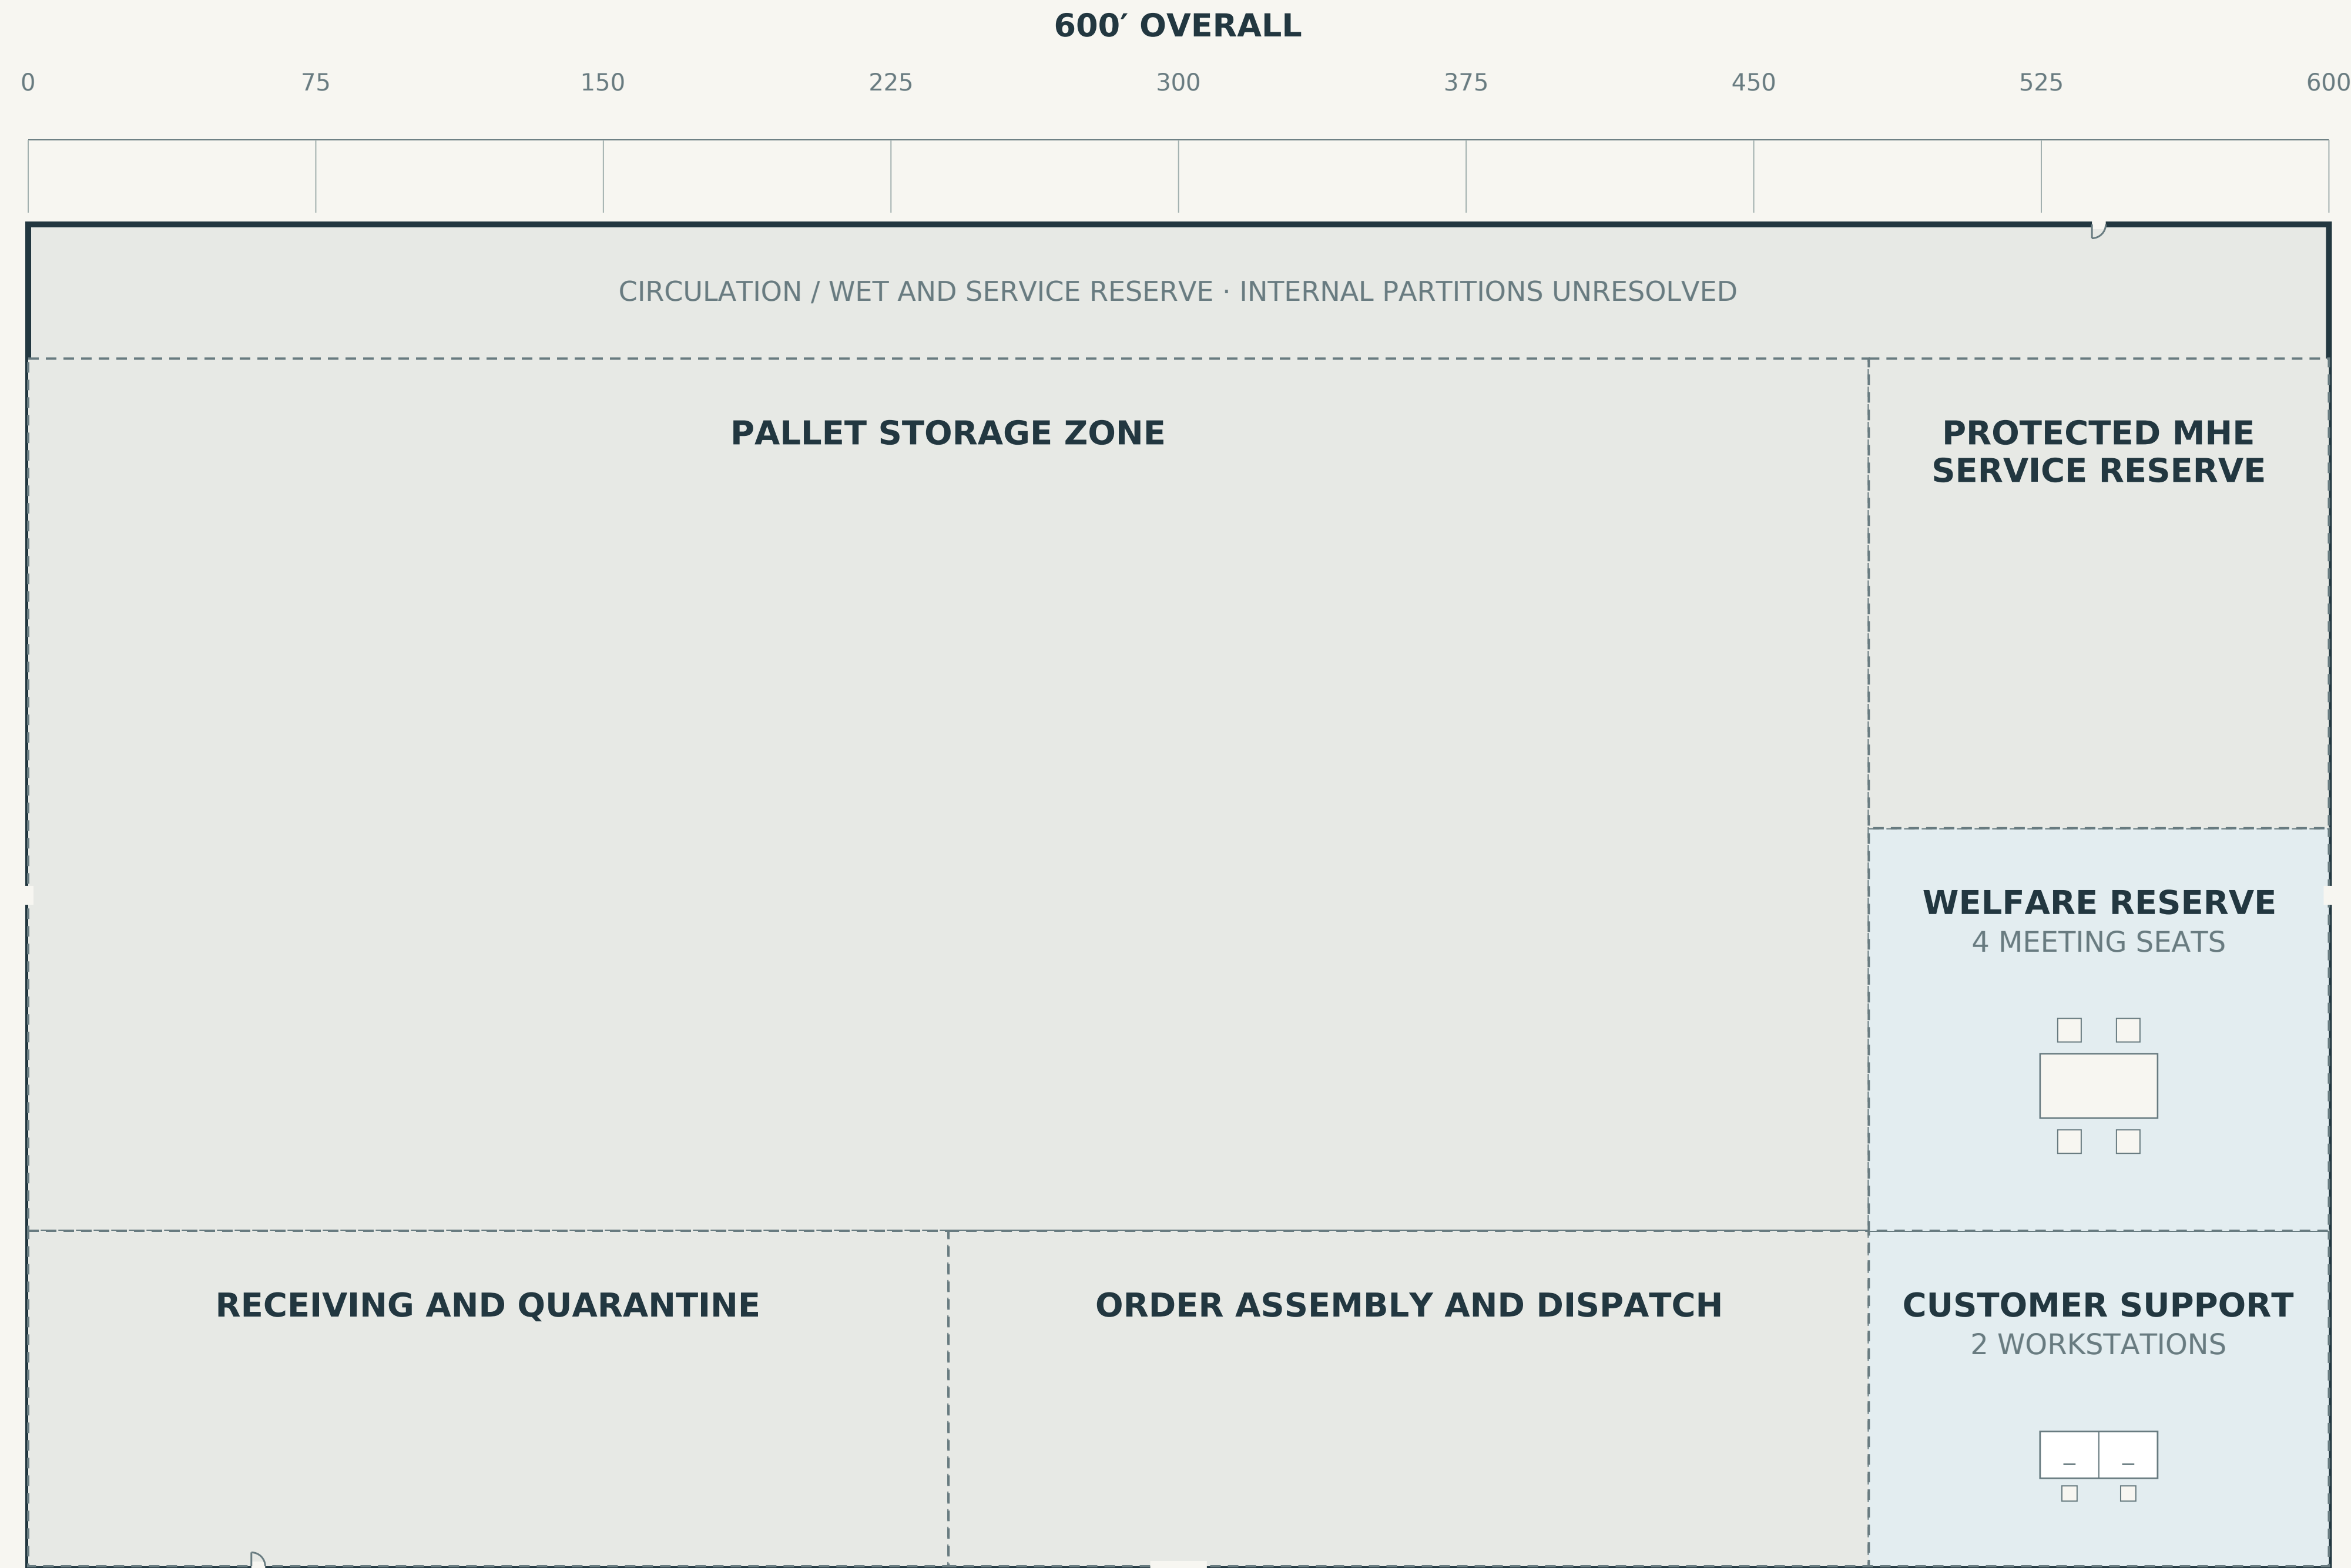

THIS FLOOR

2

FITTED WORKPLACES

210,000

GROSS SQUARE FEET

PEOPLE / CAPACITY

Planned concurrent load: 8. Fitted workplaces, meeting seats, learners and residents are separate measures; actual occupancy remains unestablished.

COORDINATED BUILDING

1 levels use the same footprint and aligned service/core positions. Rooms are local concept allocations, not an as-built survey.

ACCESS AND STATUS


Opposed perimeter exits with clear personnel paths separated from handling/vehicle zones. Detailed exit distances and protective separation unverified.

01 OPERATIONAL ZONES

Dashed lines allocate work areas, not walls or installed equipment. Internal thresholds and engineered handling paths remain unresolved.

02 PERIMETER ACCESS

Sourced openings reserve personnel and handling interfaces. The service band remains inside the gross area; final fire, utility and accessibility design requires engineering.

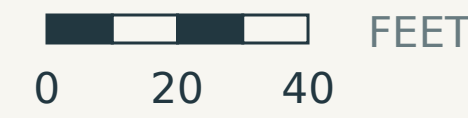

Blue: operational work / Sage: secondary program / Sand: shared and visitor areas