


CORPORATE / LEVEL 02

Product engineering and deployment • One floor shown • North is up

CONCEPT REVIEW / R02

SH-SITE-0001-A-L02 / SH-MAP-SAC-025

216' OVERALL

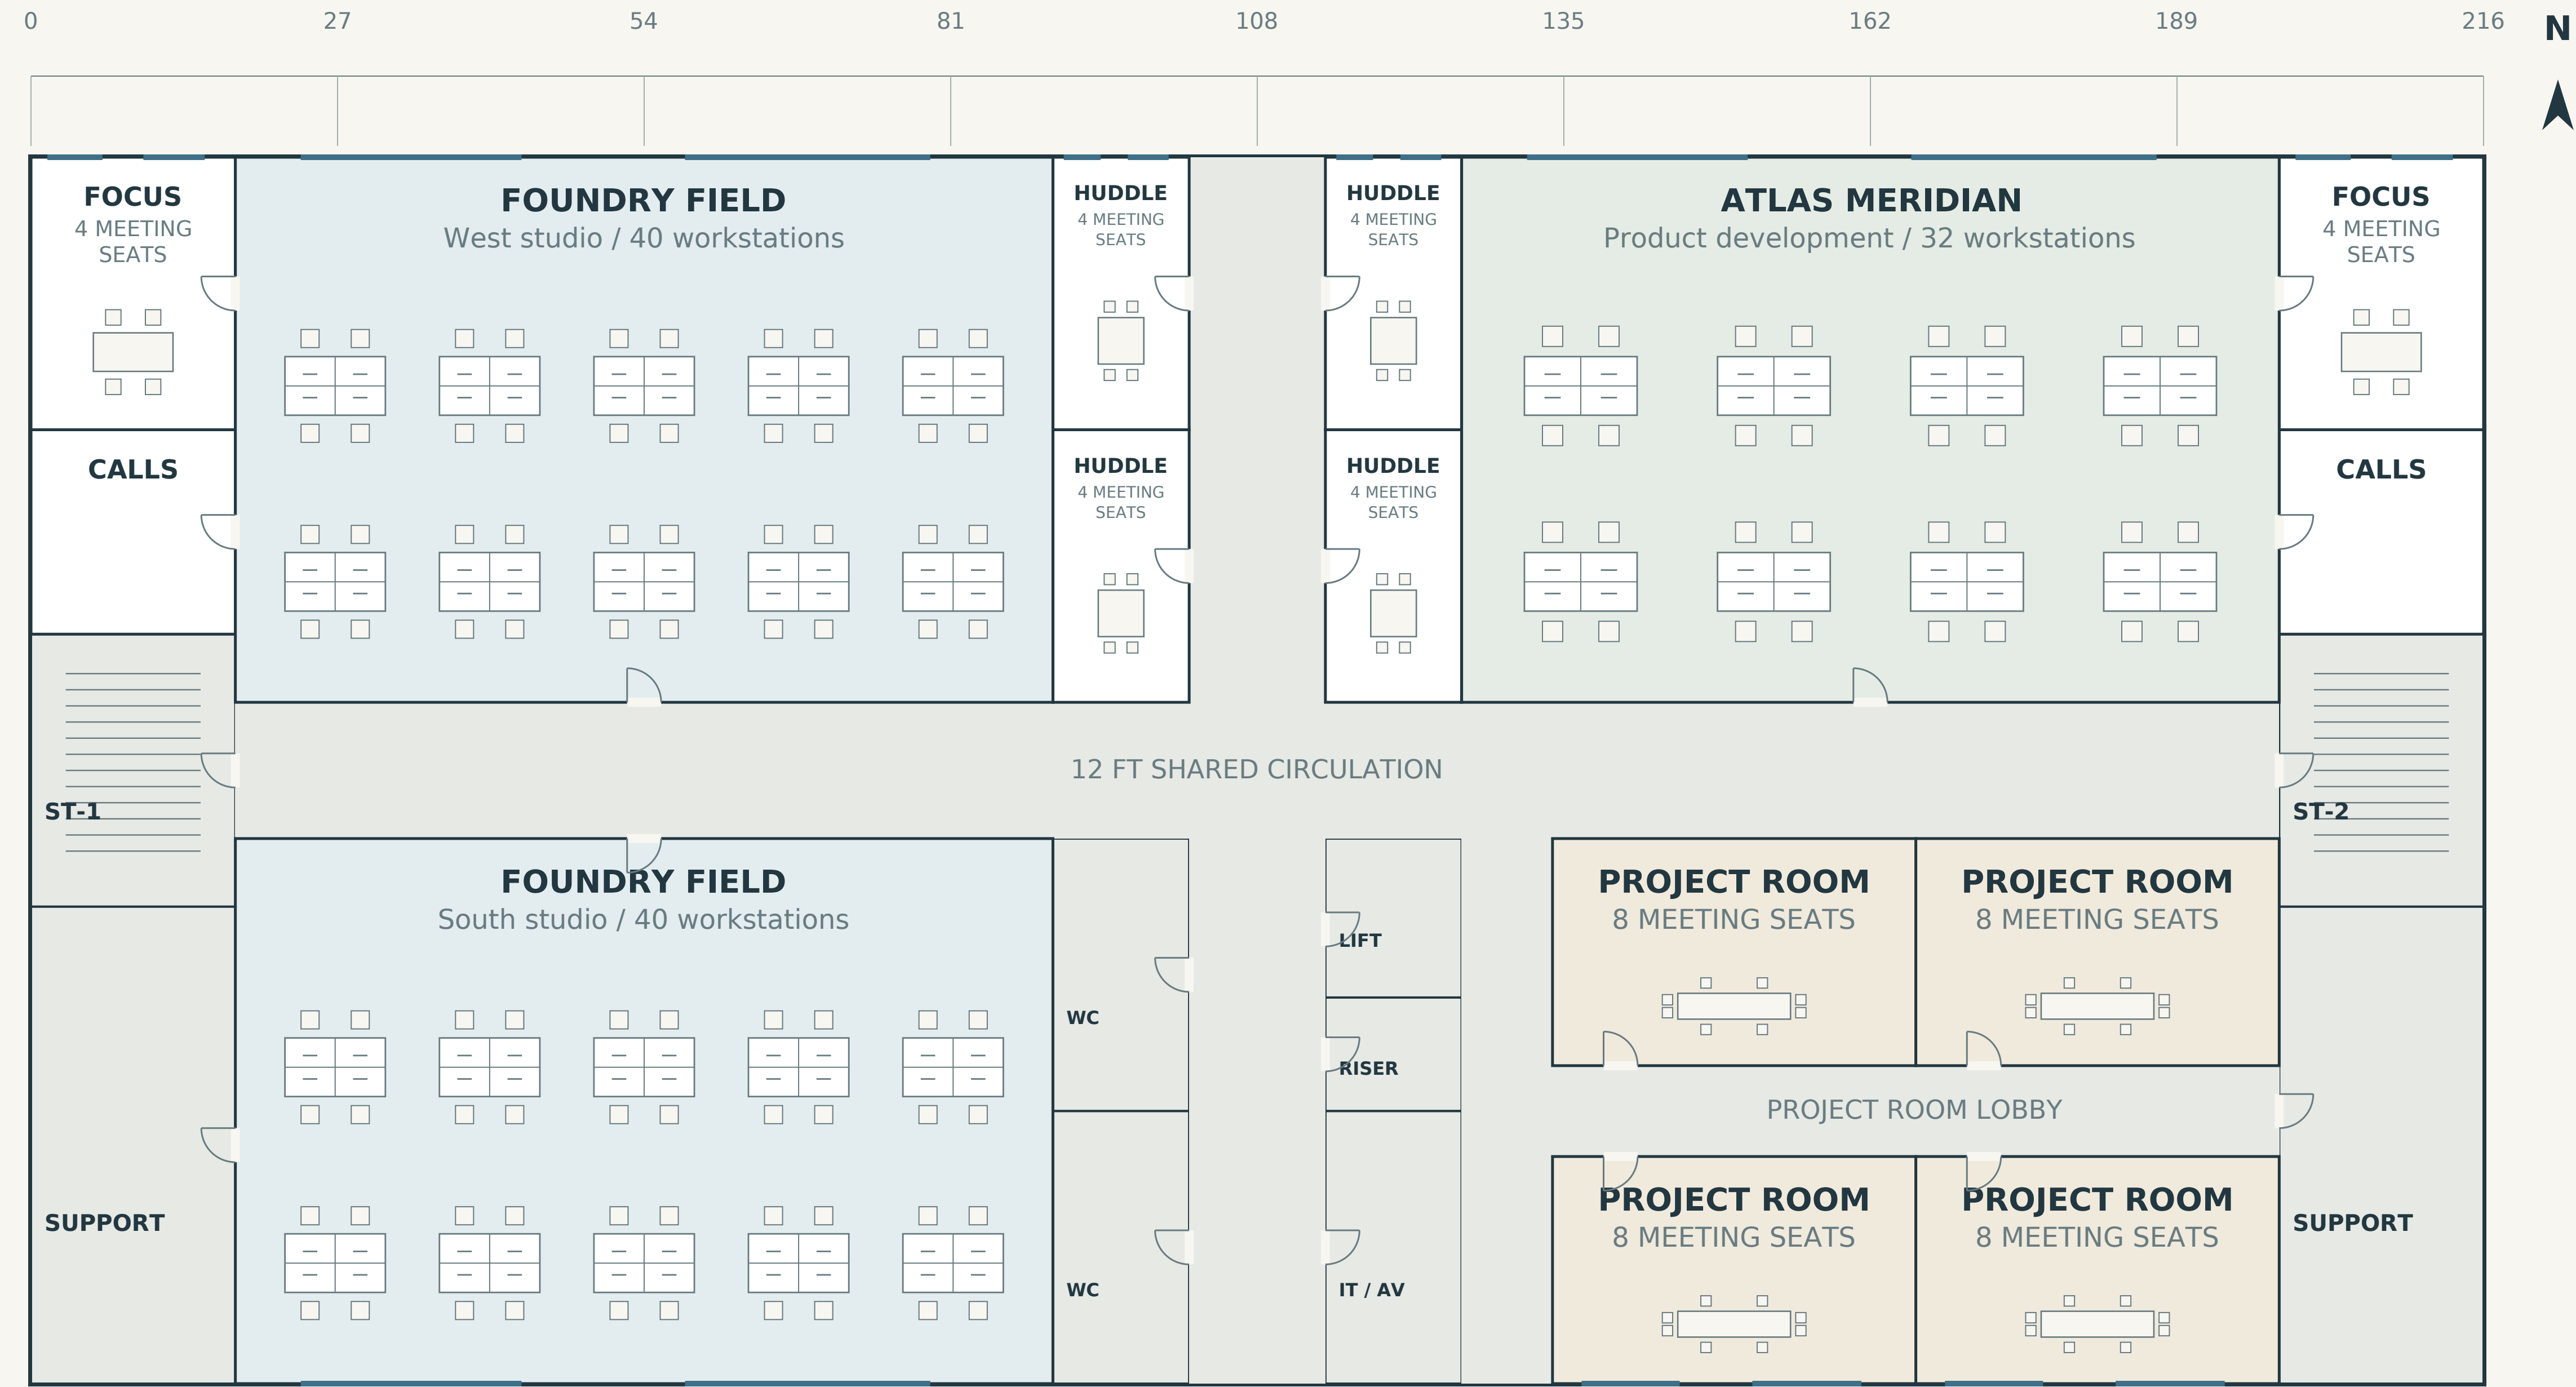

THIS FLOOR

112

FITTED WORKPLACES

23,328

GROSS SQUARE FEET

STAFF ≠ DESKS

Foundry Field: 160 modelled staff / 80 desks here. Atlas Meridian: 36 modelled staff / 32 desks here. These R01 scenario counts are not an actual employee census.

IN THE SAME BUILDING

L01: Advisory, client reception, visiting workplaces and commons. L03: corporate officers, ESS and an independently secured Internal Audit suite. Product organizations retain separate leadership.

DESIGN LOAD / STATUS


23,328 gross sq ft; 112 planned concurrent occupants. R02 concept only; actual staffing, occupancy and construction remain unestablished.

01 TEAM BOUNDARIES

Shared project rooms support joint work. Atlas retains a dedicated product organization.

02 CAMPUS CONNECTION

Visitors check in on L01. J2 and the teaching/residential precinct have their own entrances.

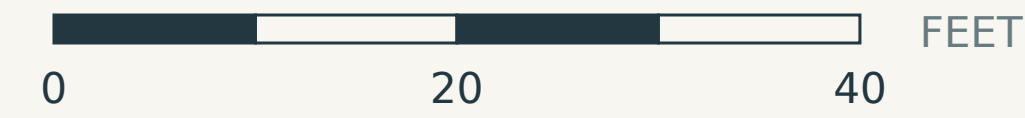

Blue: Foundry Field / Sage: Atlas Meridian / Sand: shared project rooms