


CORPORATE / LEVEL 03

Corporate officers / ESS / independent Internal Audit • One floor shown • North is up

CONCEPT REVIEW / R02

SH-SITE-0001-A-L03 / SH-MAP-SAC-026

216' OVERALL

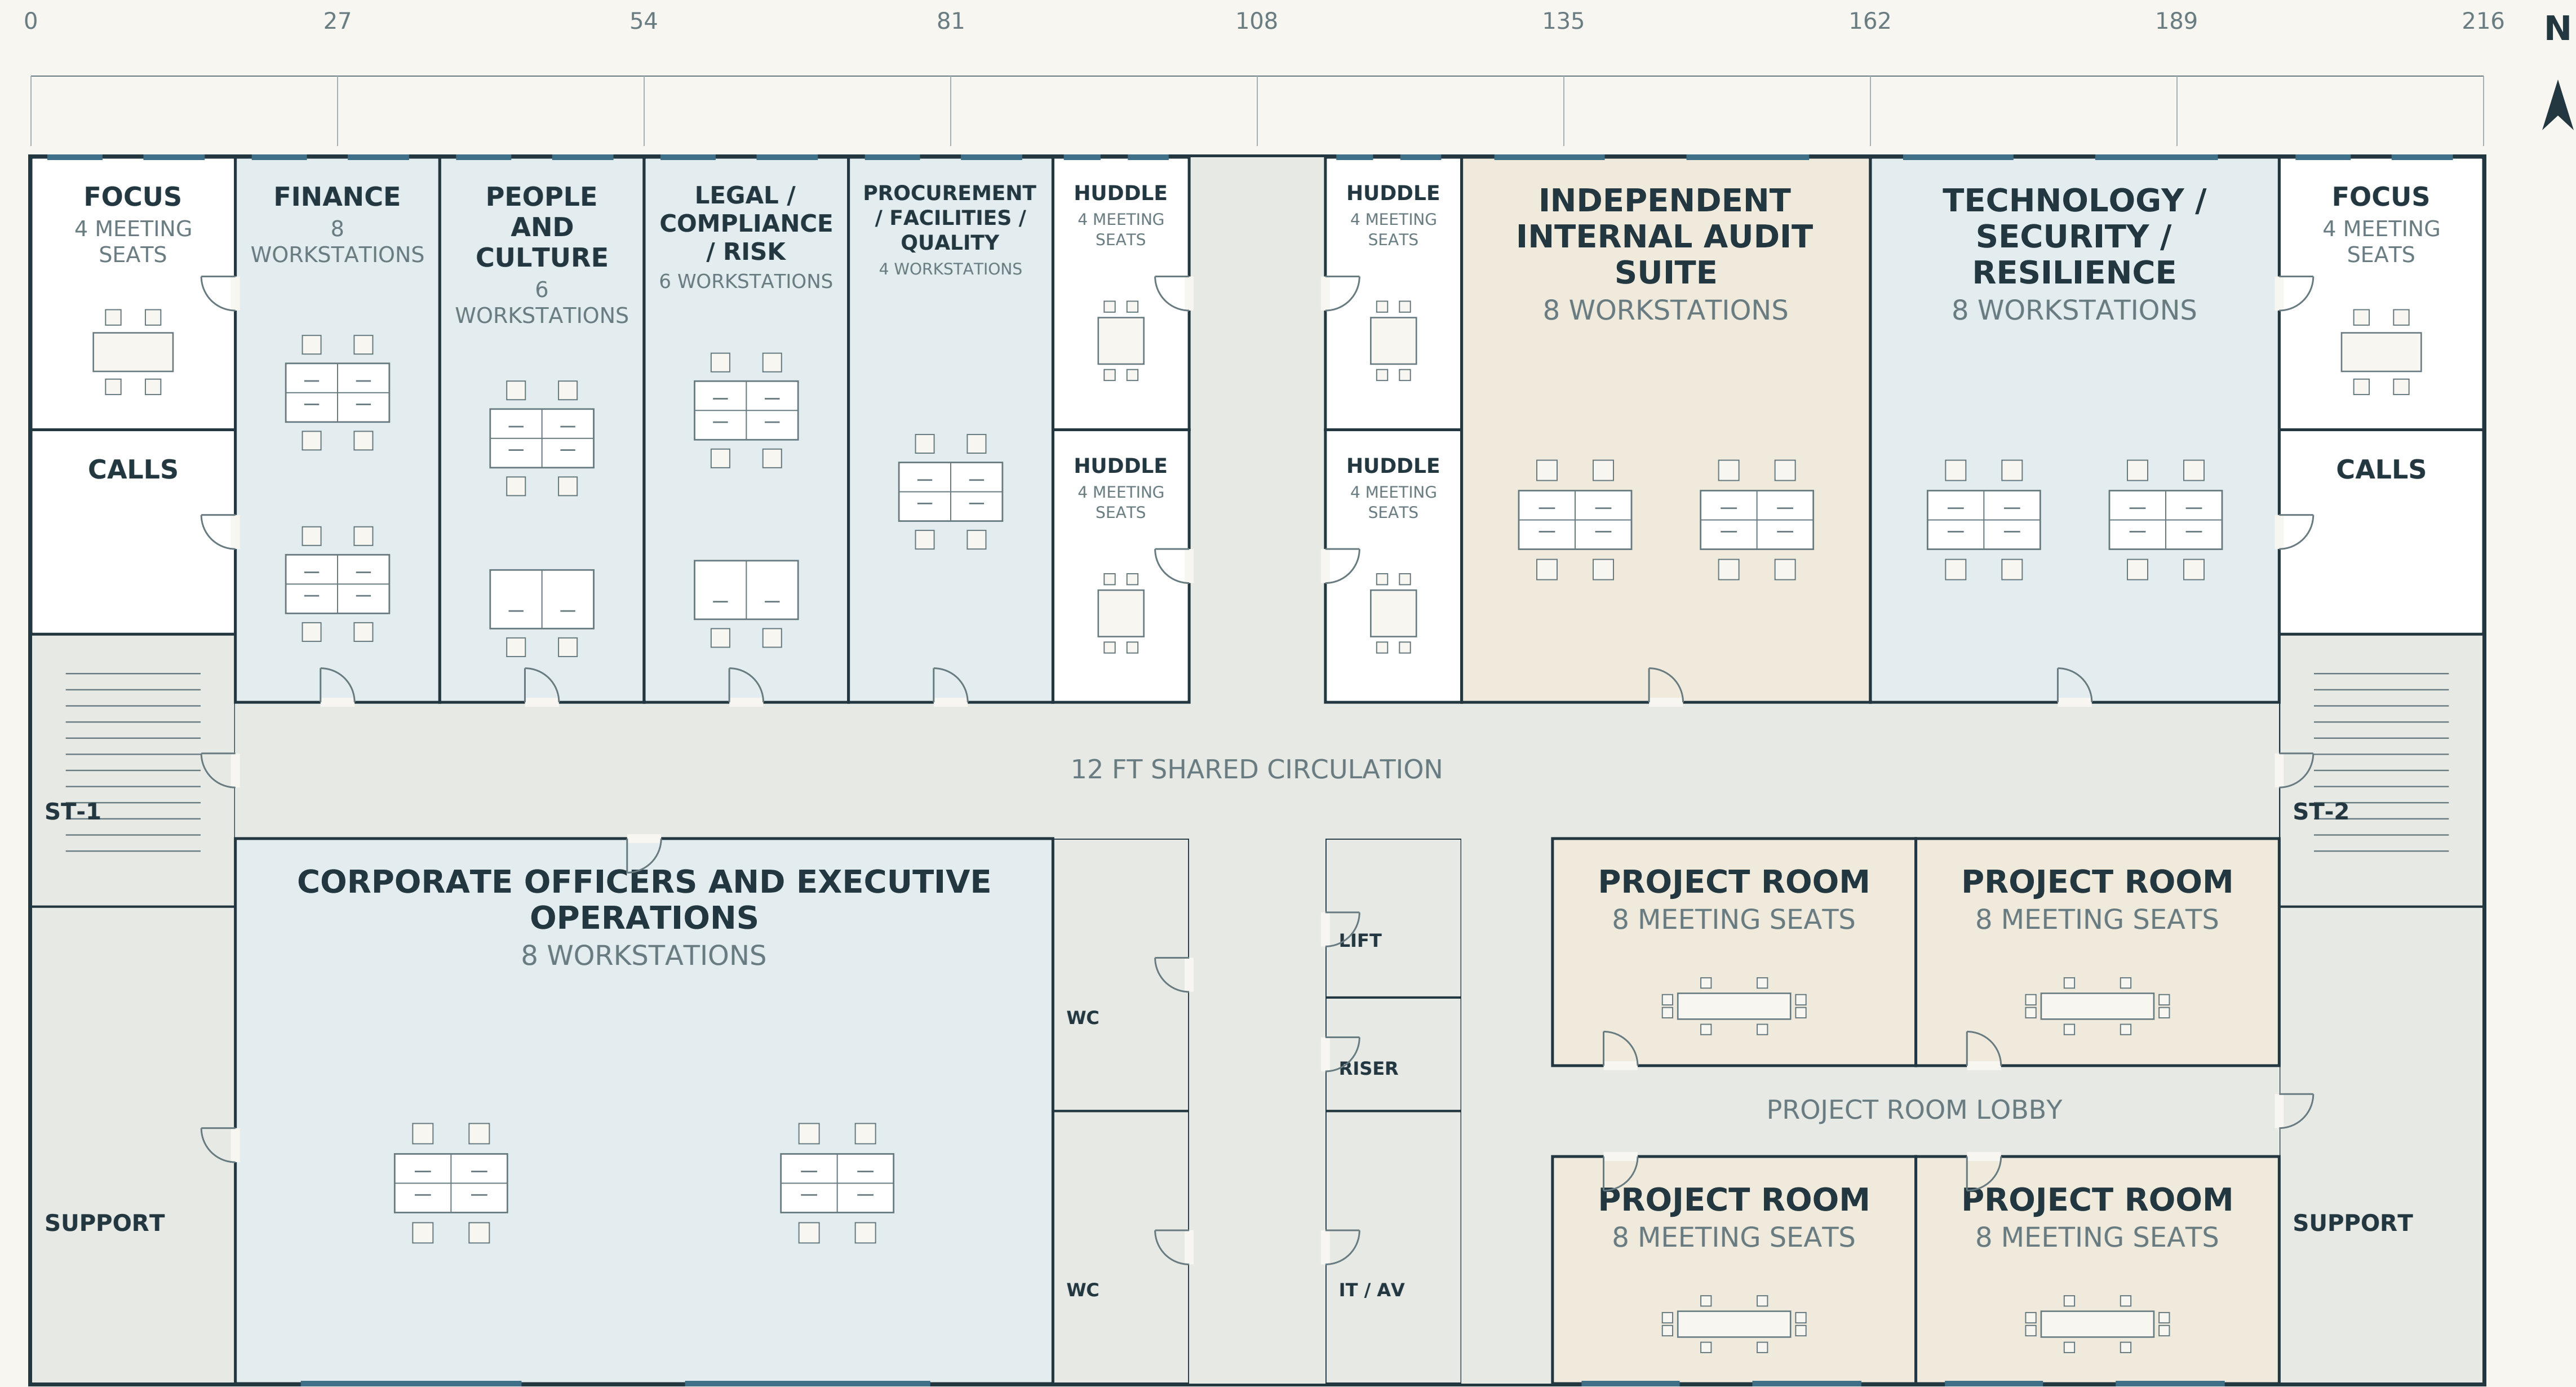

THIS FLOOR

48

FITTED WORKPLACES

23,328

GROSS SQUARE FEET

FLOOR PROGRAM

Finance • People and Culture • Legal / Compliance / Risk • Procurement / Facilities / Quality • Corporate officers and executive operations • Independent Internal Audit suite • Technology / Security / Resilience

INSTITUTIONAL BOUNDARY

Board governs, CEO directs and ESS administers shared services. Internal Audit retains independently controlled Board access; J2 and business product organizations retain their separate authority.

DESIGN LOAD / STATUS


23,328 gross sq ft; 48 planned concurrent occupants. R02 concept only; actual staffing, occupancy and construction remain unestablished.

01 SHARED CAMPUS

48 workplaces: 24 ESS professional services, 8 corporate officers/executive operations, 8 Audit and 8 Technology/Security/Resilience.

02 CONTROLLED ACCESS

Internal Audit has its own controlled entrance and Board accountability; it is not an ESS reporting unit.

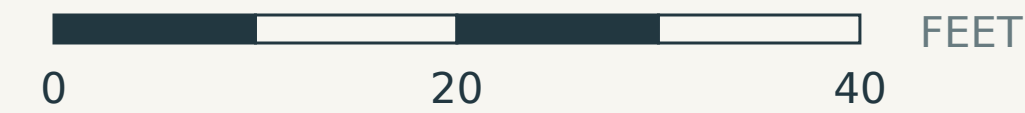

Blue: staff work / Sage: shared or independent program / Sand: visitor and project rooms